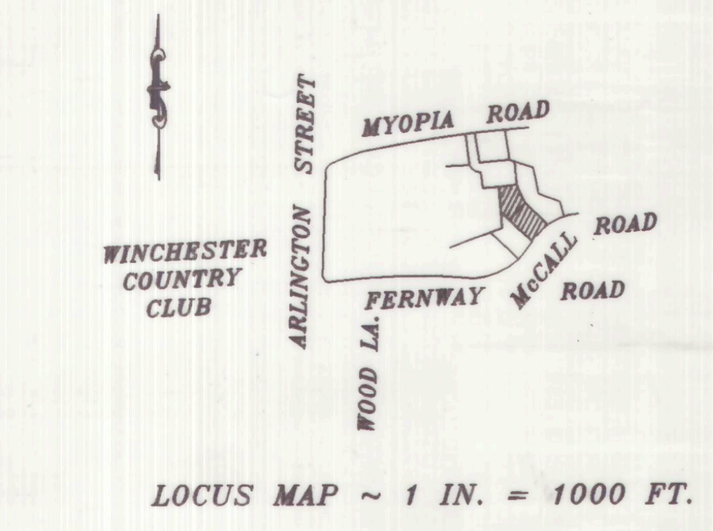
MYOPIA ROAD
ARLINGTON STREET
WINCHESTER COUNTRY CLUB
McCALL ROAD
ROAD
FERNWAY
WOOD LA.

LOCUS MAP ~ 1 IN. = 1000 FT.

11955-F


11955E
9
N/F BELANGER
N84°20'35"E
95.00'
55
5
5/8" REBAR FD
(HELD FOR LINE)
123.72'
S05°37'25"E
N07°59'47"W
84.96'
76
12
CBDH FD
80.92'
N82°21'19"W
180.01'
54
13
SBDH FD
L3
6
102.86'
S74°00'33"W
.07'
.14'
.08'
.11'
S07°46'01"E
N04°20'42"W
133.97'
146.14'
N07°39'38"W
99.26'
104.31'
S23°12'02"E
VACANT ~ LAND
NOT A BUILDABLE LOT
28
16,789.89 SF
4
L2
56
11
5/8" REBAR FD
20
N/F JOHNSTON
27
LC PLAN 11955E
N/F LOHNES
(TRUSTEE OF SCHRAFFTS CANDY LAND TRUST)
53
14
IP D
56.76'
N44°22'45"E
121.41'
86.45'
N03°47'37"W
29
36,792.57 SF 19
-16,789.89 SF 28
20,002.68 SF
165.43'
S45°37'11"E
.07'
.11'
45.50'
L4
85.00'
7
L5
DRILL HOLE
IN STONE FD
89
16
79
IP S
12/2/11
3
GLASS HSE
HI BRICK
19
BOT WD
DK
SPLIT LEVEL DWELLING #33
BOT WD
29.3'
40.2'
TOTAL FRONTAGE ~ 122.05' ~
C2
C1
57
10
5/8" REBAR FD
14'
15'
74
C7
N31°22'03"W
156.61'
18
BOT WD
19.9'
LOT WIDTH
121.41'
BITUMINOUS DRIVE
EDGE OF PAVEMENT
EDGE OF PAVEMENT
51
NF
N28°50'44"E
121.90'
L1
227.22'
N45°37'11"W
170.46'
45.50'
47.60'
S01°53'12"W
108.32'
S41°14'13"W
8
L6
63
17
SBDH FD
.20'
.03'
7.18'
.07'
.08'
DRILL HOLE
IN STONE FD
15
88
64
7.18'
77.38'
70.20'
N69°30'36"E
75.00'
67
18
N/F CHAN
S23°29'30"E
230.31'
52
IP S
12/2/11
11'
18'
2
70.00'
S36°36'10"W
58
NF
C3
N38°11'44"E
144.52'
McCALL ROAD
(PRIVATE ~ 40' WIDE)
65
C4
1
SPIKE SET
(TYPICAL)
60
9
SBDH FD
(HELD POSITION)
N79°08'19"E
59.29'
C5
62
NF
C6
73

No.	Delta	Radius	Arc Length	Chord Length	Chord Bearing
C1	16°08'55"	289.91	81.71	81.44	S44°40'38"W
C2	16°08'55"	289.91	81.71	81.44	S44°40'38"W
C3	06°36'39"	437.28	50.45	50.42	S39°54'29"W
C4	09°02'45"	437.28	69.04	68.97	S47°44'11"W
C5	13°27'45"	250.38	58.83	58.69	S58°59'26"W
C6	06°22'33"	366.80	40.82	40.80	S73°33'15"W
C7	19°58'58"	289.91	101.11	100.60	N62°44'34"E

No.	Bearing	Distance
L1	S36°36'10"W	40.34'
L2	N84°45'55"E	27.97'
L3	N12°59'54"E	19.62'
L4	N10°03'54"W	30.58'
L5	S14°18'58"W	9.55'
L6	S20°55'22"E	7.42'

SBDH	STONE BOUND WITH DRILL HOLE
CBDH	CONCRETE BOUND WITH DRILL HOLE
IP	IRON PIPE
D	FOUND DISTURBED
FD	FOUND
NF	COORDINATED SEARCH BUT NOT FOUND
S	SET

ASSESSOR MAPS 122, 123 & 135
PARCEL 20-64 (LC LOT 27)
PARCEL 20-57 (LC LOT 18)
PARCEL 20-79 (LC LOT 19)

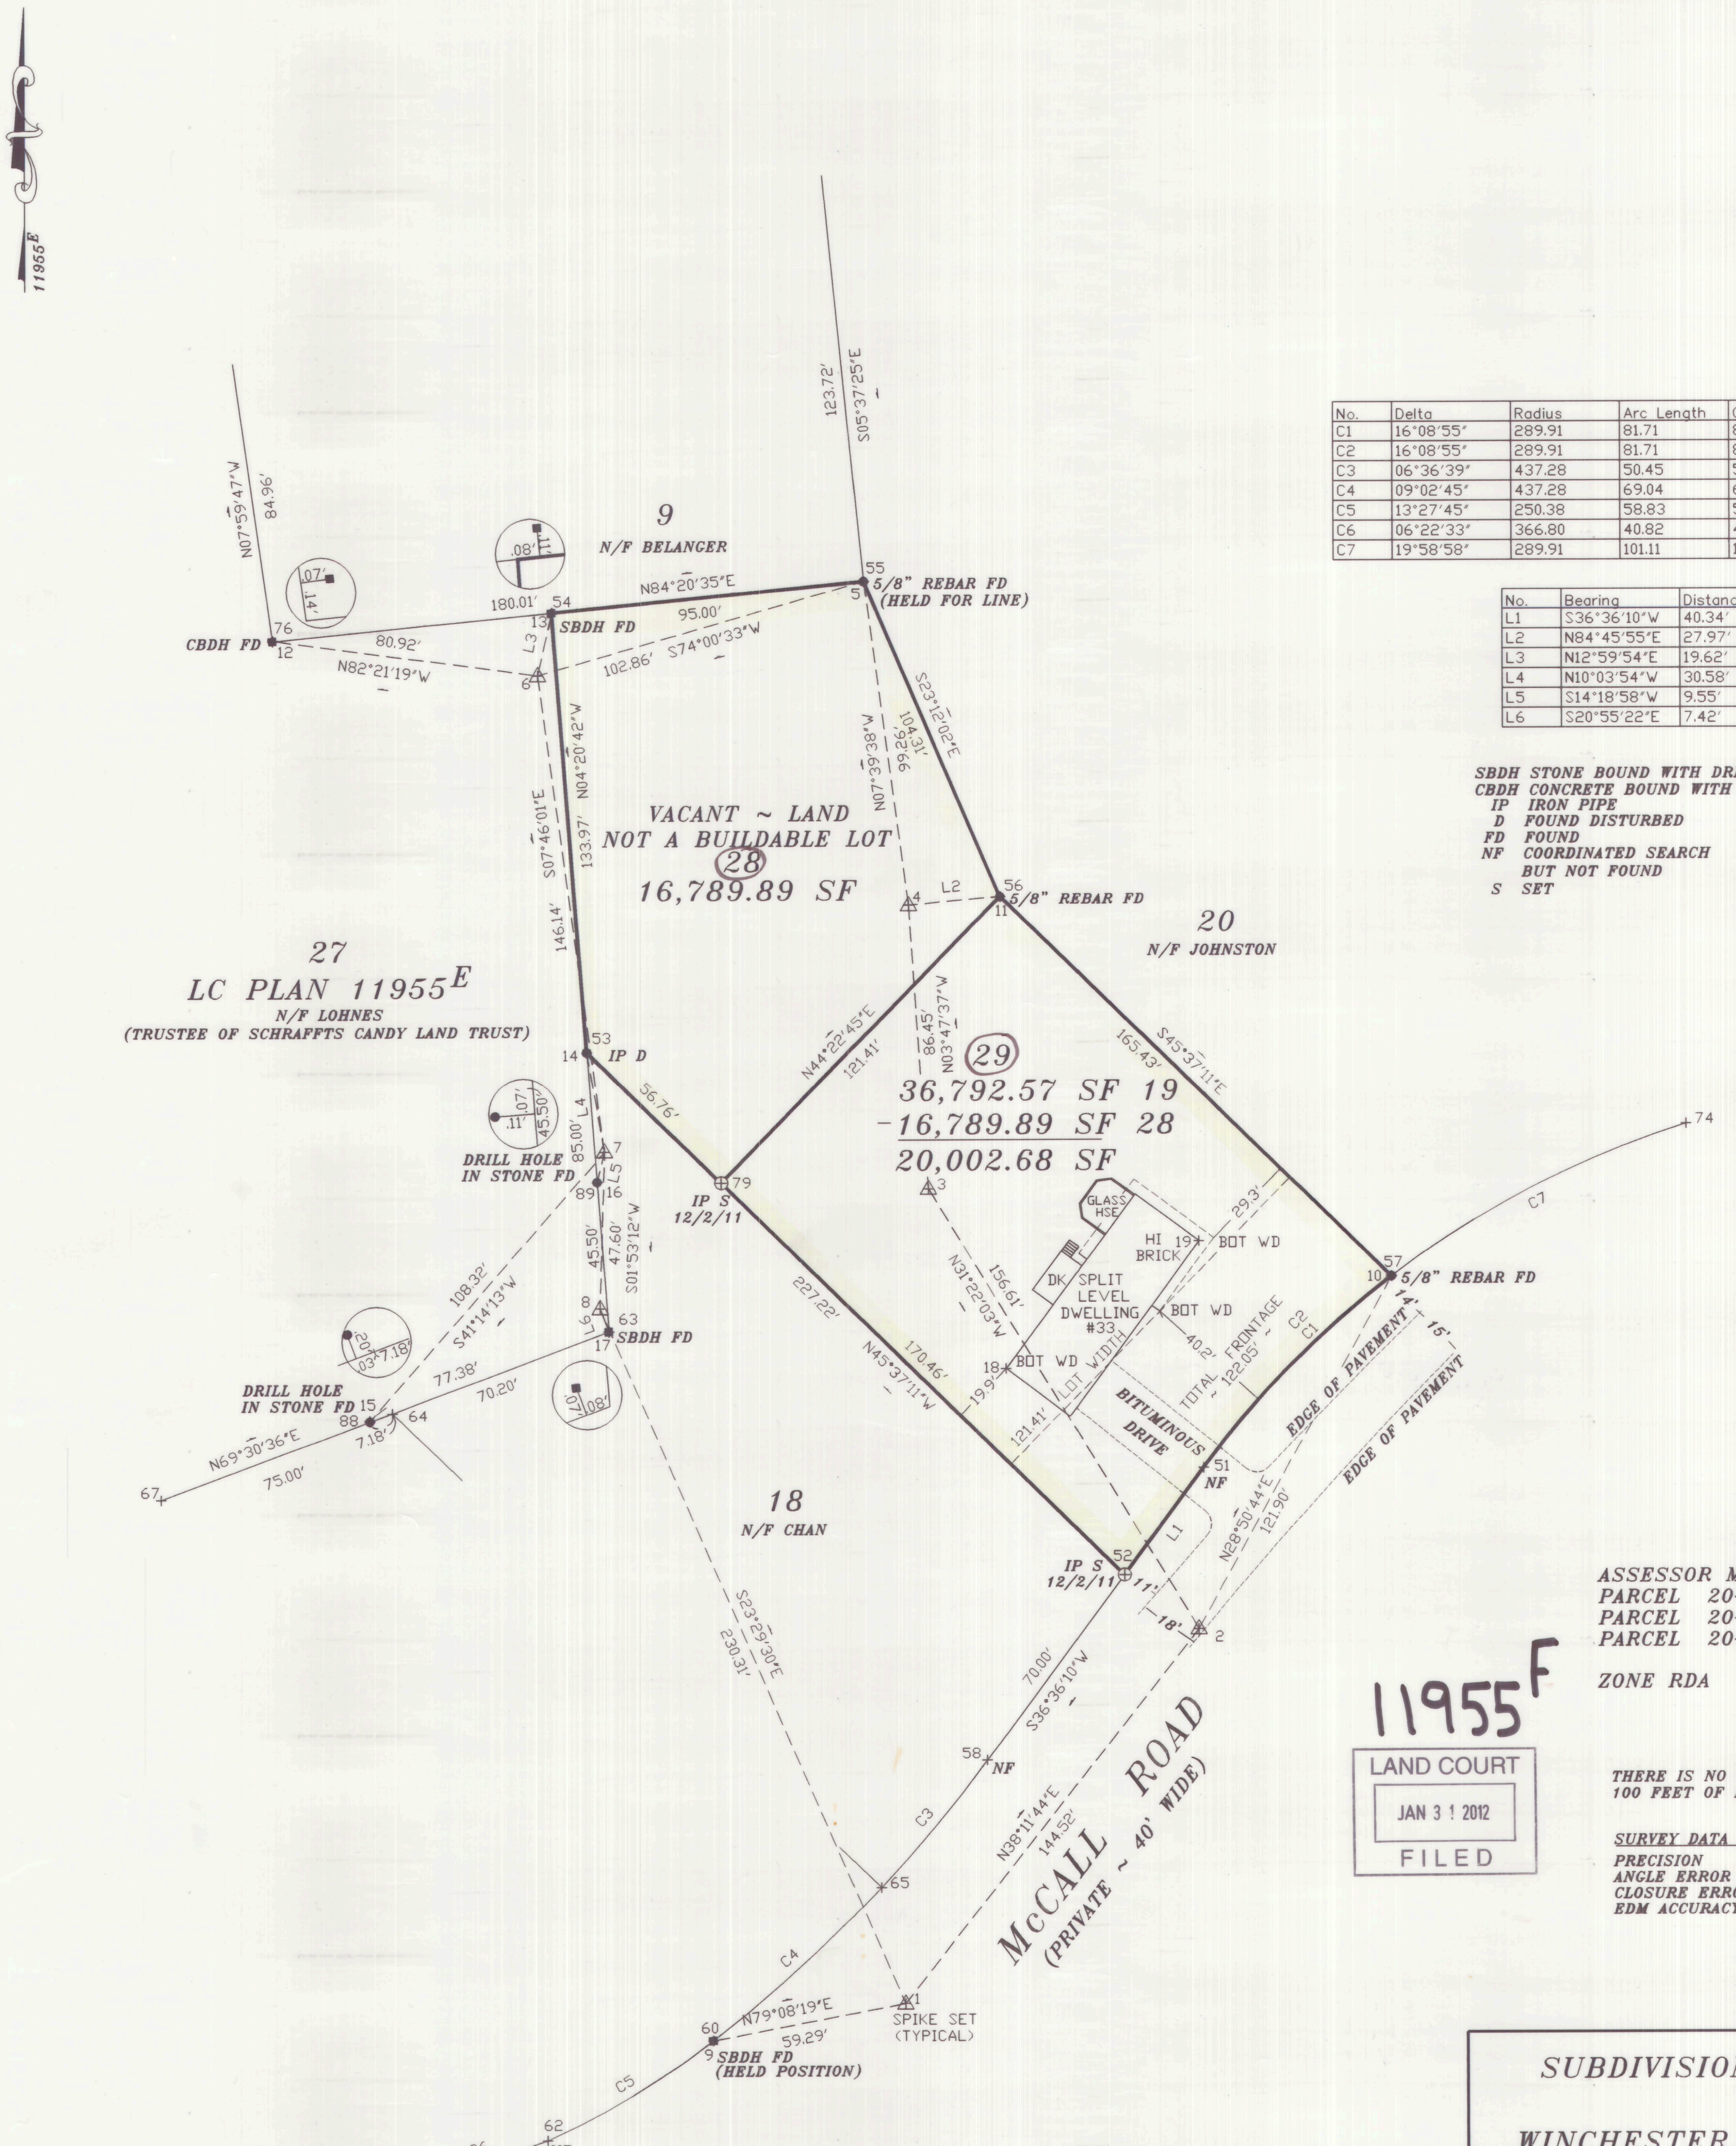ZONE RDA

11955F

LAND COURT
JAN 3 1 2012
FILED

THERE IS NO WETLAND ON, OR WITHIN 100 FEET OF LOT 19.

SURVEY DATA ~ SOKKIA SET 610

PRECISION	1:224,219
ANGLE ERROR	00°00'05.5"
CLOSURE ERROR	0.0045
EDM ACCURACY	±(2+2ppm X D)mm

THE PURPOSE OF THIS PLAN IS TO SPLIT THE CURRENT LOT 19 OWNED BY THE UNIVERSITY OF FLORIDA, INC. INTO TWO WITH THE FRONT PORTION ON McCALL ROAD TO BECOME LOT 29 AND RETAINED BY THE UNIVERSITY OF FLORIDA, INC. AND THE REAR PORTION TO BECOME LOT 28 AND BE RETAINED BY PAUL R. LOHNES, OWNER OF LOT 27.

SUBDIVISION PLAN OF LAND IN WINCHESTER, MASSACHUSETTS

LOT 19
LAND COURT PLAN 11955D

ROD D. CARTER, SURVEYOR

JANUARY 10, 2012

OWNER: UNIVERSITY OF FLORIDA FOUNDATION, INC.
P.O. BOX 14425 GAINESVILLE, FLORIDA 32604
DEED BOOK 1396 PAGE 62 CERTIFICATE 248233

PREPARED FOR: PAUL R. LOHNES

GRAPHIC SCALE

30 0 15 30 60 120

9.2M 0 15M 30M 36.6M

(IN FEET)
1 inch = 30 ft.

ROD CARTER ASSOCIATES
LAND SURVEYORS
15 PLEASANT STREET
UPTON, MA 01568
508-529-7632

31438C

ROD D. CARTER #34301

I CERTIFY THAT AS OF THE DATE OF THIS SURVEY, THE MONUMENTS CONTROLLING PRIOR PLANS ARE IN THE GROUND AS SHOWN AND DESCRIBED HEREON. I FURTHER CERTIFY THAT ANY ADDITIONAL MONUMENTS SHOWN HEREON HAVE BEEN SET IN ACCORDANCE WITH THE LAND COURT INSTRUCTIONS OF 2006 AS OF THE DATE OF THIS SURVEY.

I CERTIFY THAT THIS PLAN WAS DRAWN FROM AN ACTUAL SURVEY MADE ON THE GROUND IN ACCORDANCE WITH THE LAND COURT INSTRUCTIONS OF 2006 ON OR BETWEEN OCTOBER 25, 2011 AND DECEMBER 2, 2011.

Rod D. Carter 1/10/2012
ROD. D. CARTER, PLS DATE

APPROVAL UNDER THE SUBDIVISION CONTROL LAW NOT REQUIRED.
01- 26. 2012
Tim Bitter
Elizabeth M Cragan
Mary McMurray Solon
Maureen I Meister

WINCHESTER PLANNING BOARD

"THE BOARD'S ENDORSEMENT OF THE PLAN AS NOT REQUIRING APPROVAL UNDER THE SUBDIVISION CONTROL LAW DOES NOT GIVE LOTS OR PARCELS ANY STANDING UNDER THE TOWN OF WINCHESTER ZONING BYLAW."

11955-F