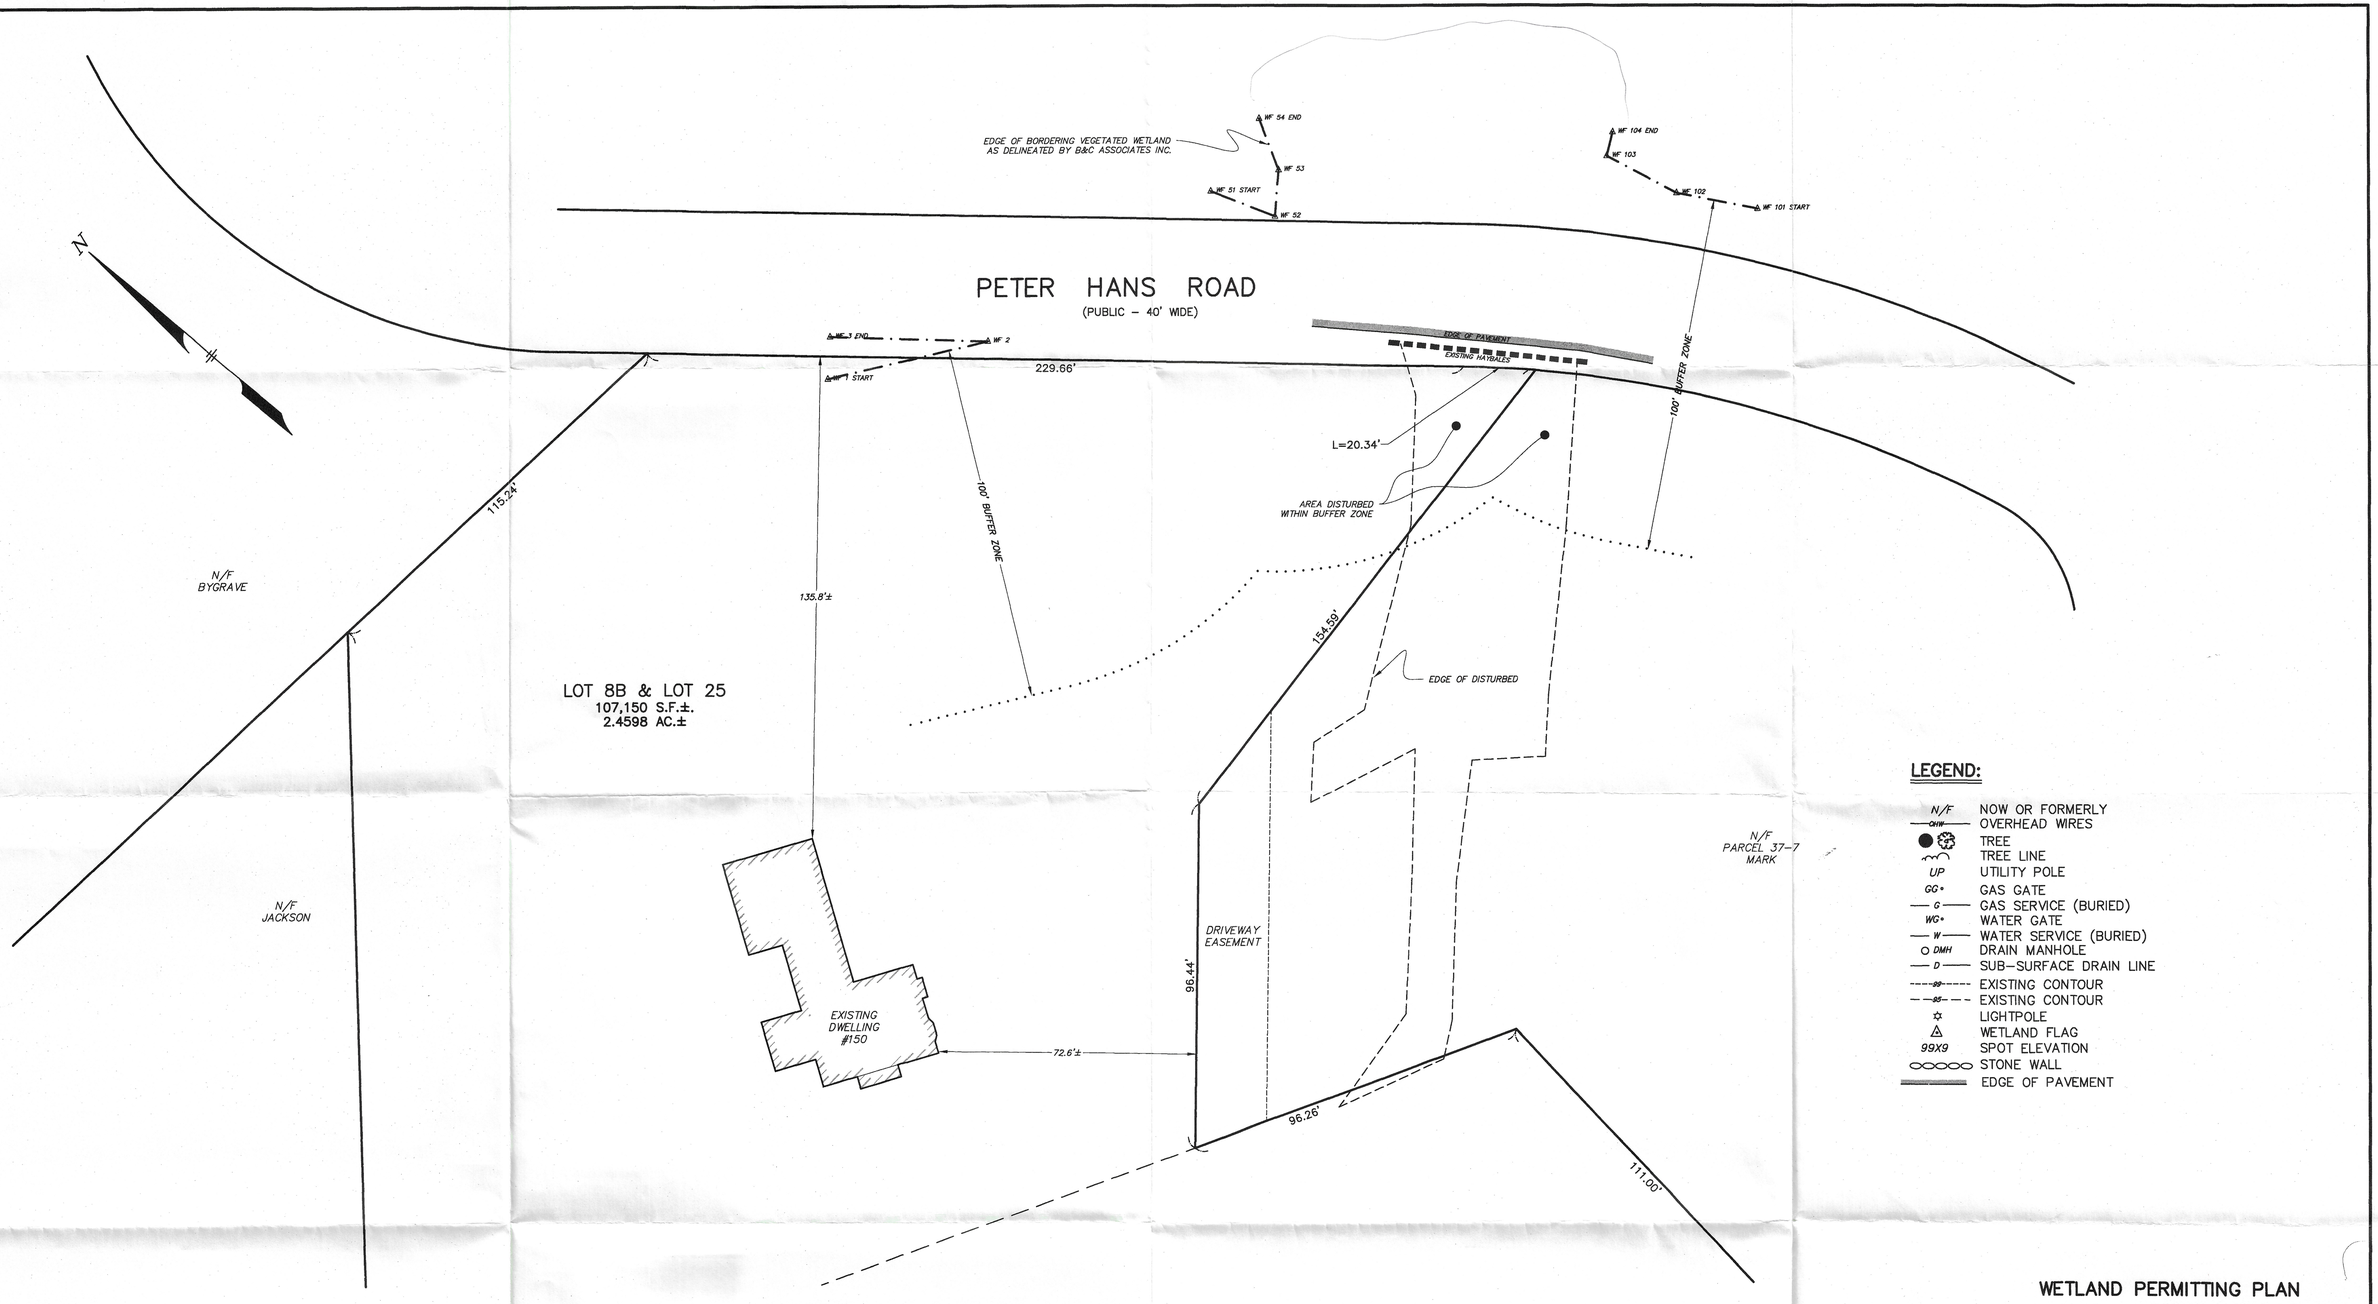



## LEGEND:

| | |
|---|---|
| N/F | NOW OR FORMERLY |
| OHW | OVERHEAD WIRES |
| | TREE |
| | TREE LINE |
| UP | UTILITY POLE |
| GG• | GAS GATE |
| G | GAS SERVICE (BURIED) |
| WG• | WATER GATE |
| W | WATER SERVICE (BURIED) |
| DMH | DRAIN MANHOLE |
| D | SUB-SURFACE DRAIN LINE |
| 99 | EXISTING CONTOUR |
| 95 | EXISTING CONTOUR |
| | LIGHTPOLE |
| | WETLAND FLAG |
| 99X9 | SPOT ELEVATION |
| | STONE WALL |
| | EDGE OF PAVEMENT |

## UTILITY NOTE:

ALL UNDERGROUND UTILITIES SHOWN HERE WERE COMPILED ACCORDING TO AVAILABLE RECORD PLANS FROM VARIOUS UTILITY COMPANIES AND PUBLIC AGENCIES AND ARE APPROXIMATE ONLY. ACTUAL LOCATIONS MUST BE DETERMINED IN THE FIELD BEFORE DESIGNING, EXCAVATING, BLASTING, INSTALLING, BACKFILLING, GRADING, PAVEMENT RESTORATION OR REPAIRING. ALL UTILITY COMPANIES, PUBLIC AND PRIVATE, MUST BE CONTACTED INCLUDING THOSE IN CONTROL OF UTILITIES NOT SHOWN ON THIS PLAN. SEE CHAPTER 370, ACTS OF 1963 MASS. WE ASSUME NO RESPONSIBILITY FOR DAMAGES INCURRED AS A RESULT OF UTILITIES OMITTED OR INACCURATELY SHOWN. BEFORE PLANNING FUTURE CONNECTIONS THE APPROPRIATE PUBLIC UTILITY ENGINEERING DEPARTMENT MUST BE CONSULTED. DIG SAFE TELEPHONE No. 1-888-344-7233.

## ZONING DISTRICT

RESIDENCE B

## DATUM

ELEVATIONS SHOWN ON THIS PLAN REFER TO AN ASSUMED BASE.

COMMONWEALTH OF MASSACHUSETTS
JOSEPH MARCH
# 36984
PROFESSIONAL LAND SURVEYOR

# WETLAND PERMITTING PLAN
IN
# CARLISLE, MASSACHUSETTS
(MIDDLESEX COUNTY)

FOR: VON ROESGEN
SCALE: 1"=20' MARCH 14, 2016

**STAMSKI AND MCNARY, INC.**
1000 MAIN STREET ACTON, MASSACHUSETTS
*ENGINEERING – PLANNING – SURVEYING*

0 10 20 40 60 80 FT

(2006 WPP.dwg) 150 Peter Hans Road SM-2006