Form LCE-S-3. 4M-11-61-931709

Ctf. 114182 Book 701 Page 39


# SUBDIVISION PLAN OF LAND IN WINCHESTER

11955D

See Key Plan of Case No. 11955 in Land Reg. Plan Dept.

George E. Hayes, Surveyor

January 17, 1964

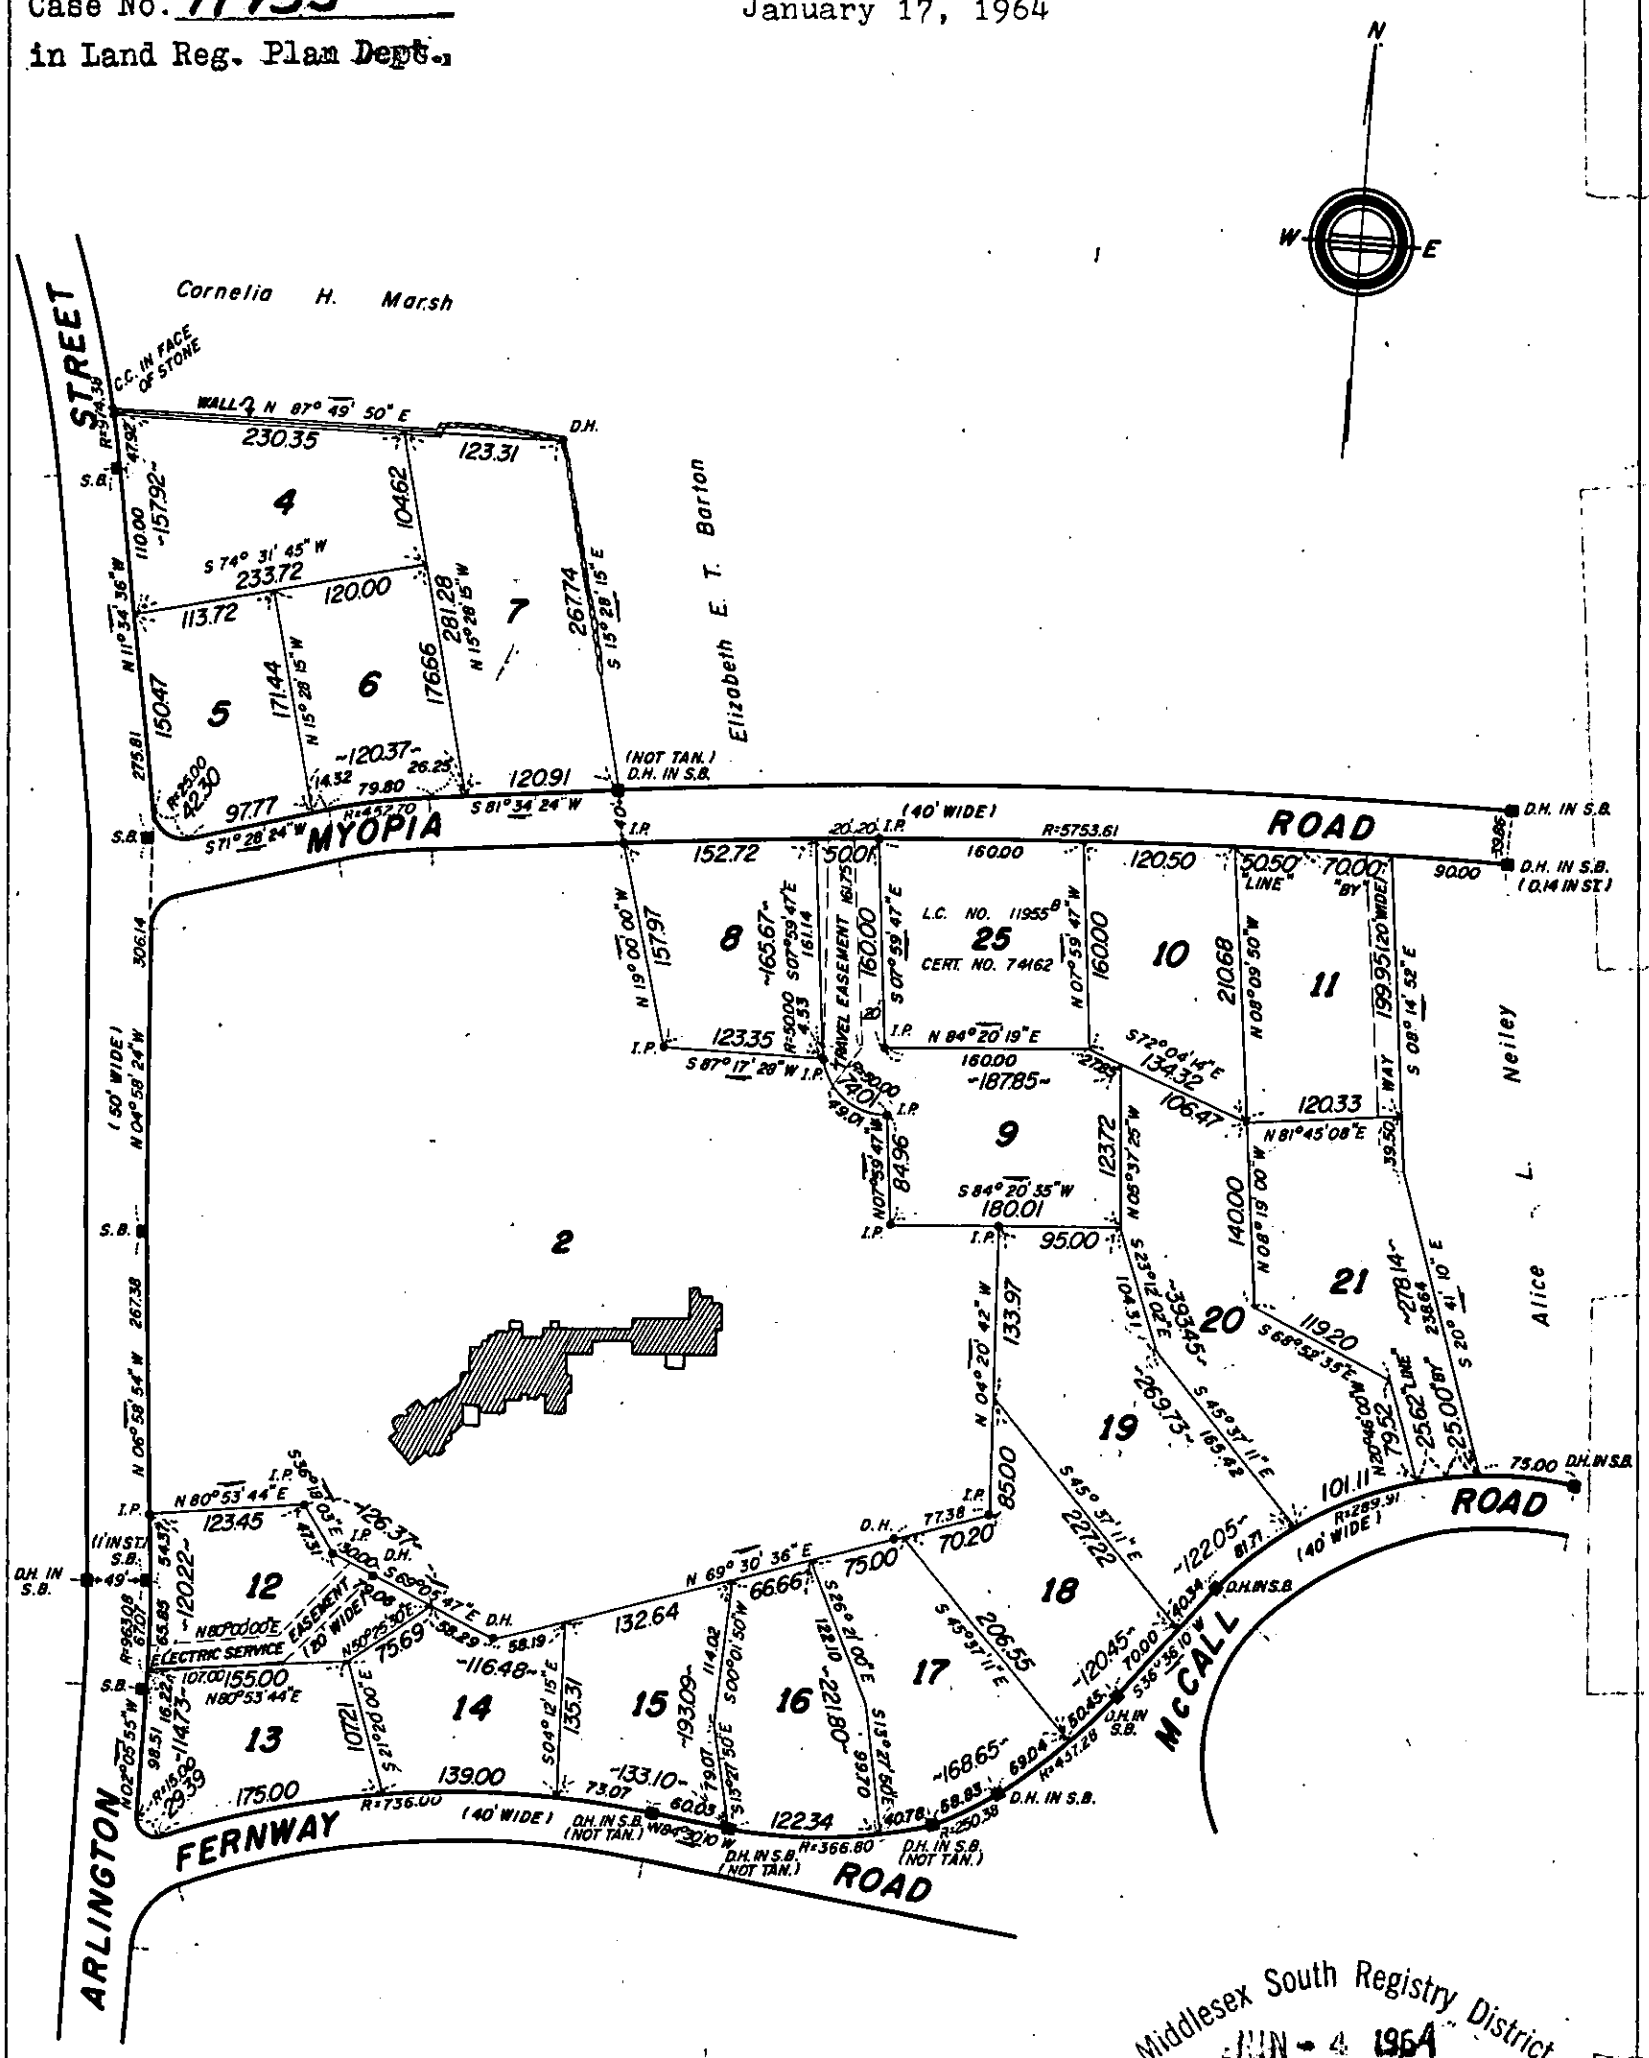


Middlesex South Registry District
JUN - 4 1964

RECEIVED FOR REGISTRATION
9 O'CLOCK 55 M a M
fd. 2.00.

Subdivision of Lots 1 & 3
Shown on Plan 11955C
Filed with Cert. of Title No. .....
South Registry District of Middlesex County.

*Separate certificates of title may be issued for land shown hereon as lots 4 thru 21 inclusive*
*By the Court.*

Maryann M. Daly
Recorder.

February 7, 1964

RJL

*Copy of part of plan filed in*
*LAND REGISTRATION OFFICE*
*February 7, 1964*
*Scale of this plan 150 feet to an inch*
*C.M. Anderson, Engineer for Court*