I-13643

AUG 16 1994

CARLISLE PLANNING BOARD

PLANNING BOARD APPROVAL NOT REQUIRED UNDER SUBDIVISION CONTROL LAW.

DATE: Aug 8, 1994

I CERTIFY THAT THIS ACTUAL SURVEY WAS MADE ON THE GROUND IN ACCORDANCE WITH THE LANDCOURT INSTRUCTIONS OF 1989 BETWEEN APRIL 18, 1994 AND JULY 8, 1994

DATE: 8-4-1994

COMMONWEALTH OF MASSACHUSETTS — RICHARD J. LUDWIG No. 29835 — REGISTERED PROFESSIONAL LAND SURVEYOR

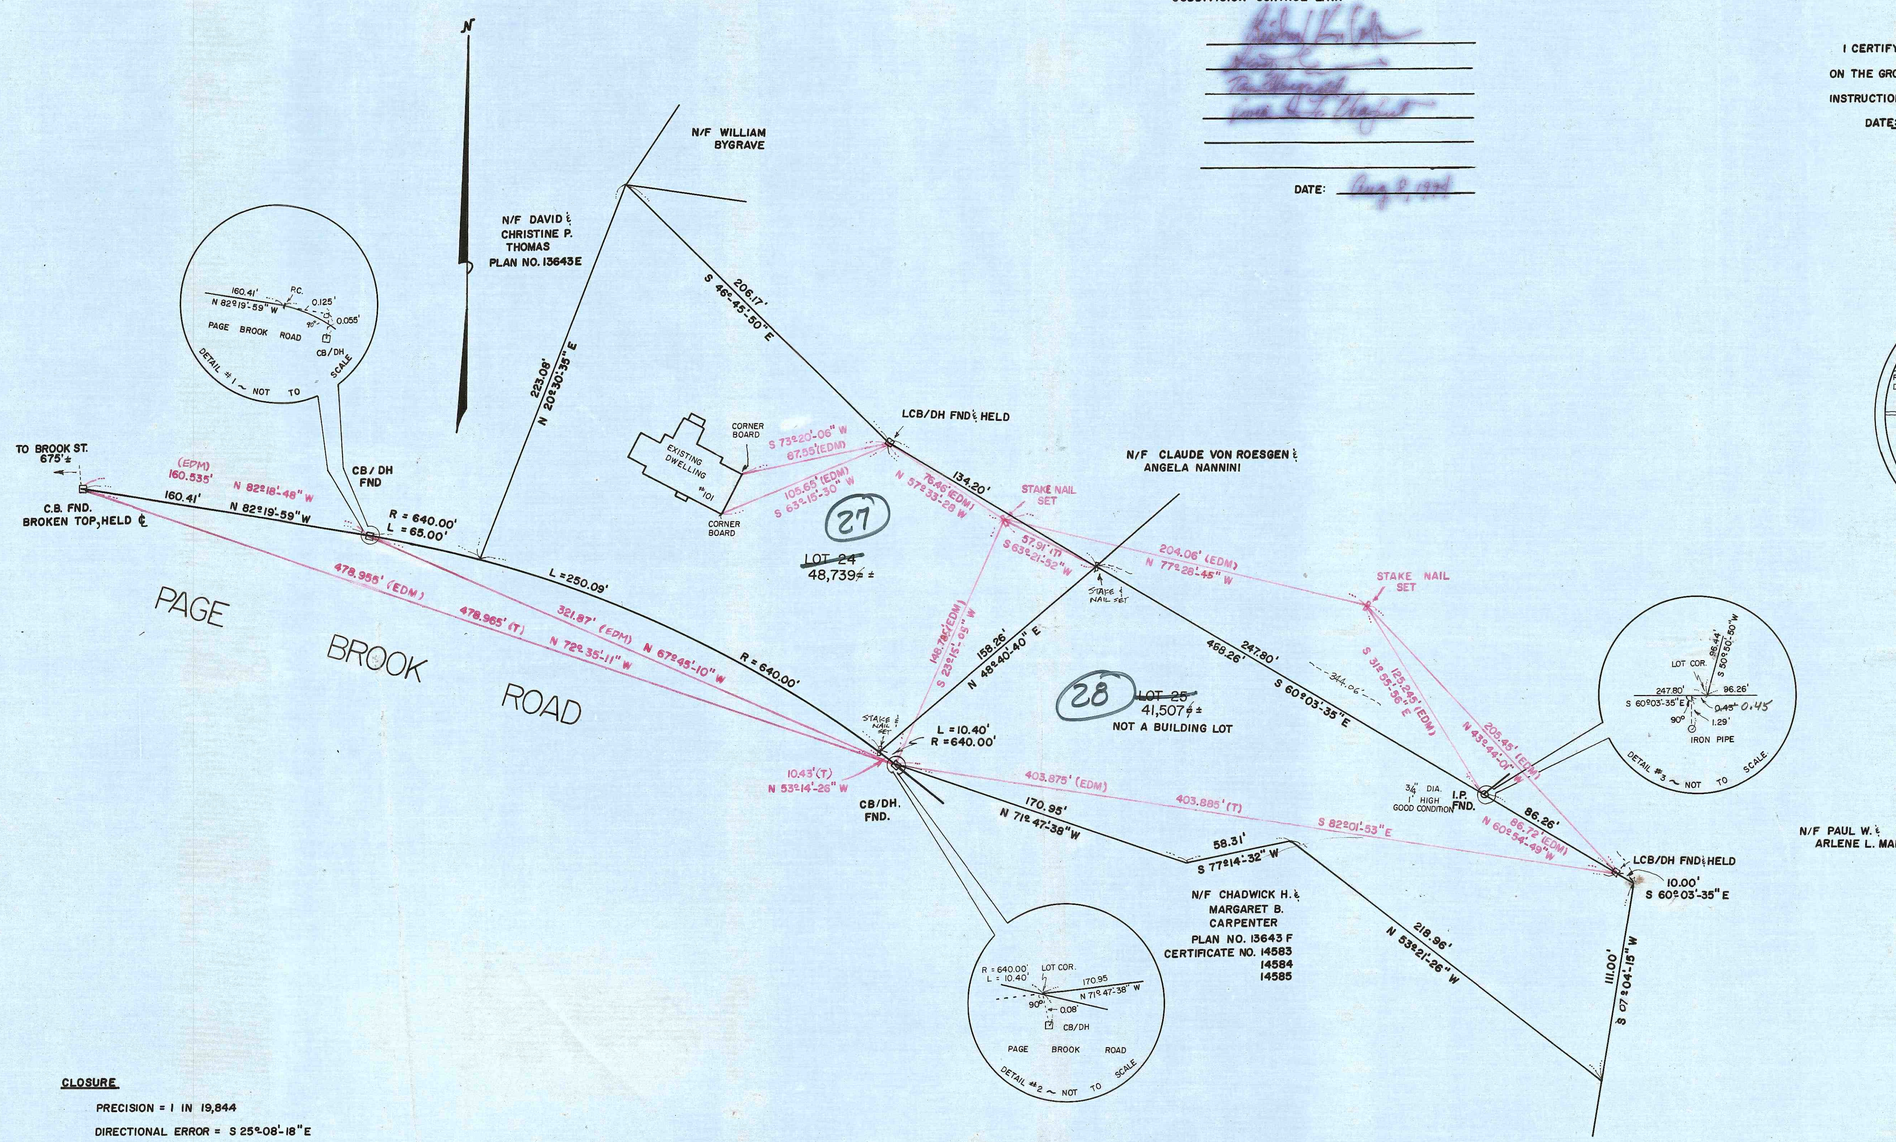

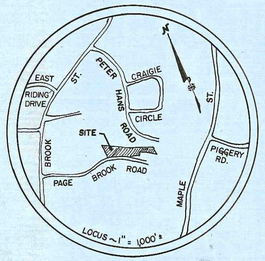

CLOSURE

PRECISION = 1 IN 19,844

DIRECTIONAL ERROR = S 25°-08'-18" E

LINEAR ERROR = 0.048'

EDM ACCURACY = ±(5MM.+ 5PPM.)

13643 I

LAND COURT
AUG 12 1994
FILED

40 0 40 80 120

PLAN	LAND
CARLISLE,	MASS.
SCALE: 1" = 40'	DATE JULY 29, 1994	PLAN # 94-042

PREPARED FOR:
ROBERT & LORRAINE STONE
101 PAGE BROOK RD.
CARLISLE, MASS. 01741

PREPARED BY:
RICHARD J. LUDWIG & ASSOC.
378 LITTLETON RD.
CHELMSFORD, MASS 01824
(508) 256-6616

SURVEYOR: RICHARD J. LUDWIG (#29835)

PREP: RJL JR | CHECK: RJL | DRAFT: STL

AUG 16 1994

13643-I